
NOTE:
REFER TO PRECAST MANUFACTURERS DRAWINGS FOR DETAILS OF PRECAST AND STARTER BARS.

NOTE:
REFER TO DESIGN REPORT FOR STONE COMPACTION REQUIREMENTS.

NOTES:
REFER TO SITE SECTIONS AND SI REPORT FOR FURTHER DETAILS/LEVELS.

DRAWING TO BE READ IN CONJUNCTION WITH CIVIL & STRUCTURAL SPECIFICATION.

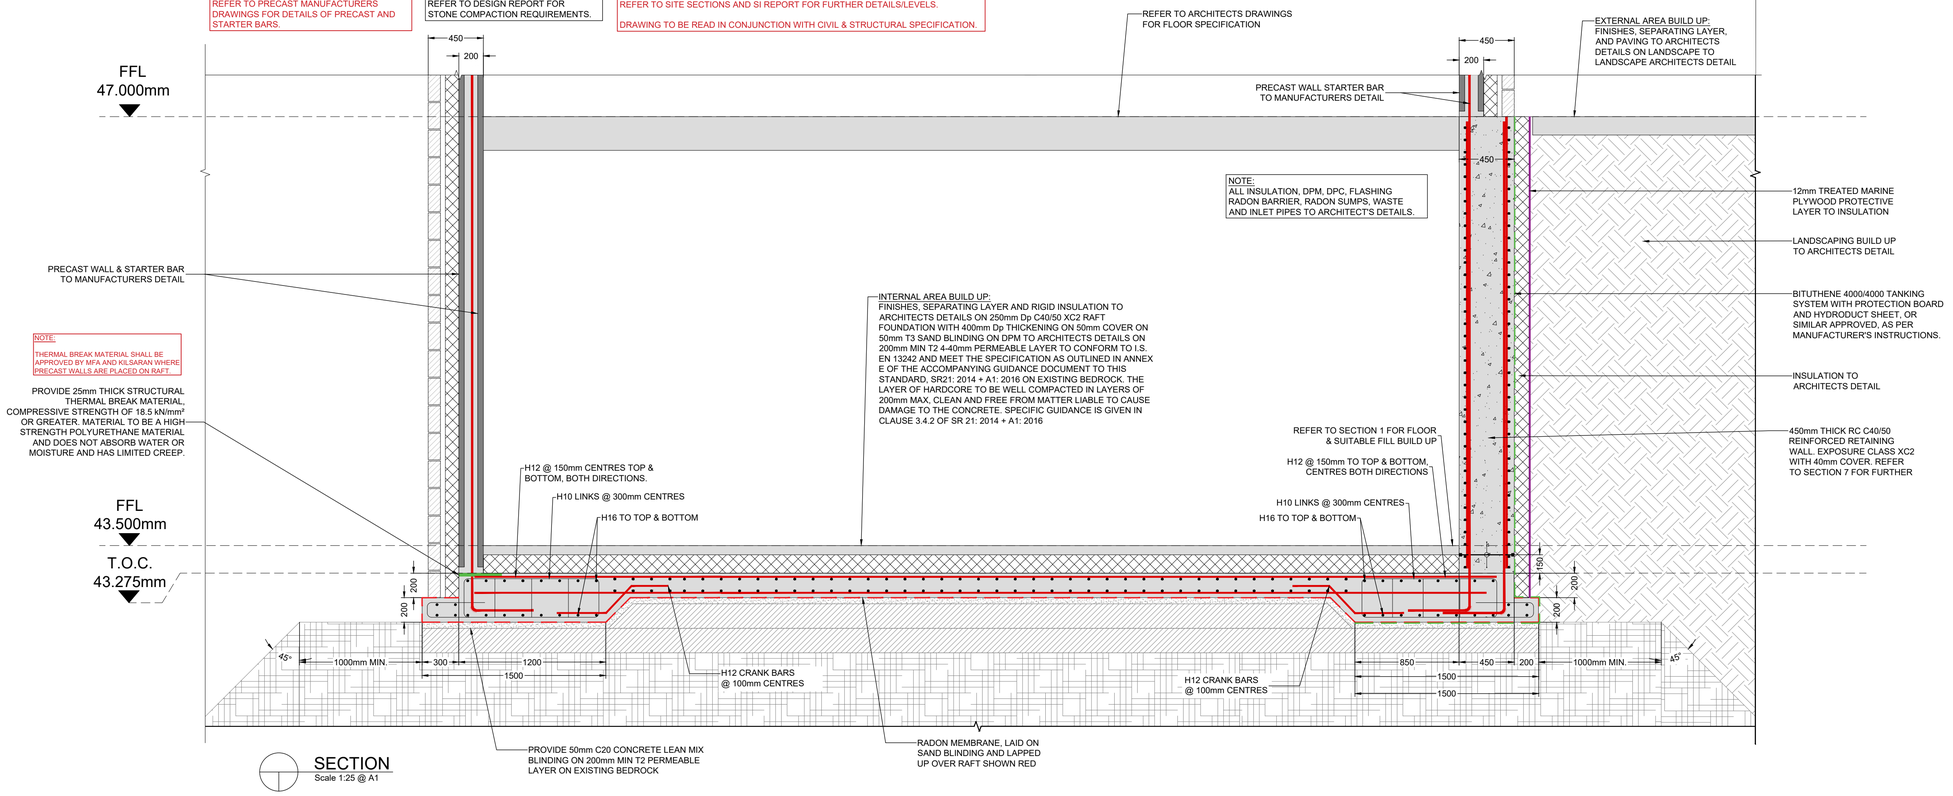


SECTION
Scale 1:25 @ A1

NOTE:
REFER TO PRECAST MANUFACTURERS DRAWINGS FOR DETAILS OF PRECAST AND STARTER BARS.

NOTE:
REFER TO DESIGN REPORT FOR STONE COMPACTION REQUIREMENTS.

NOTES:
REFER TO SITE SECTIONS AND SI REPORT FOR FURTHER DETAILS/LEVELS.

DRAWING TO BE READ IN CONJUNCTION WITH CIVIL & STRUCTURAL SPECIFICATION.

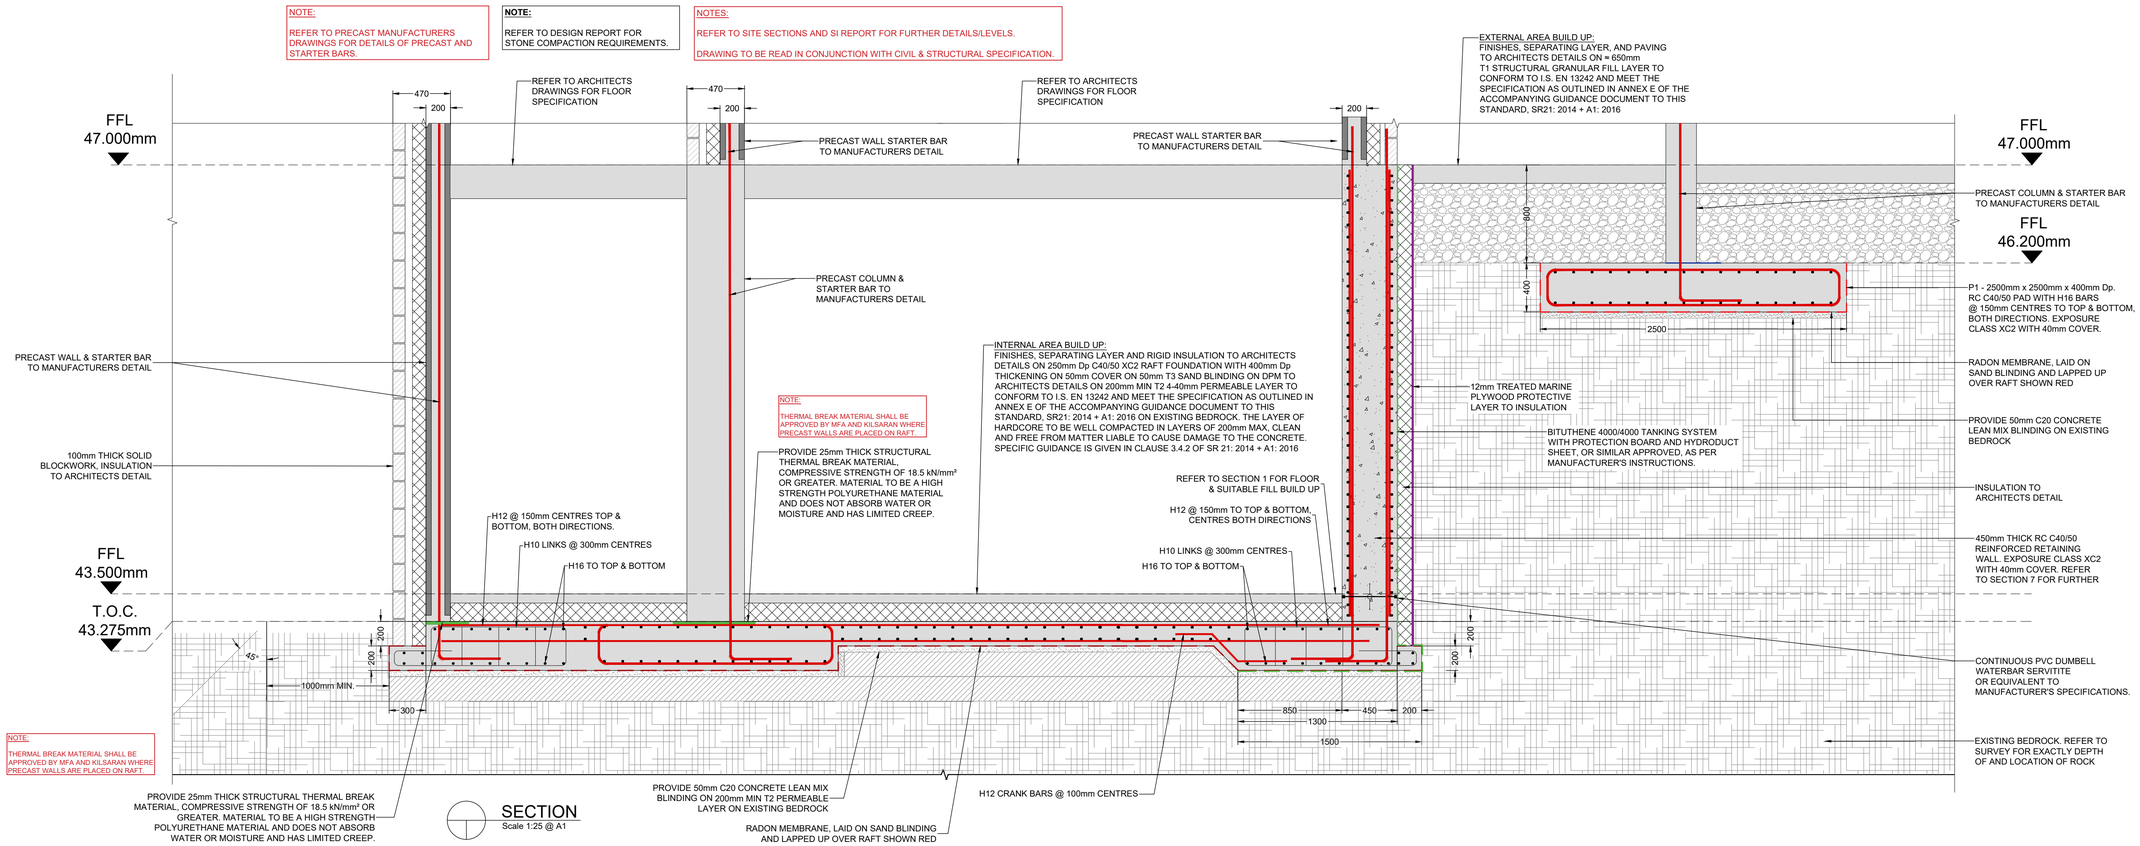

SECTION
Scale 1:25 @ A1