

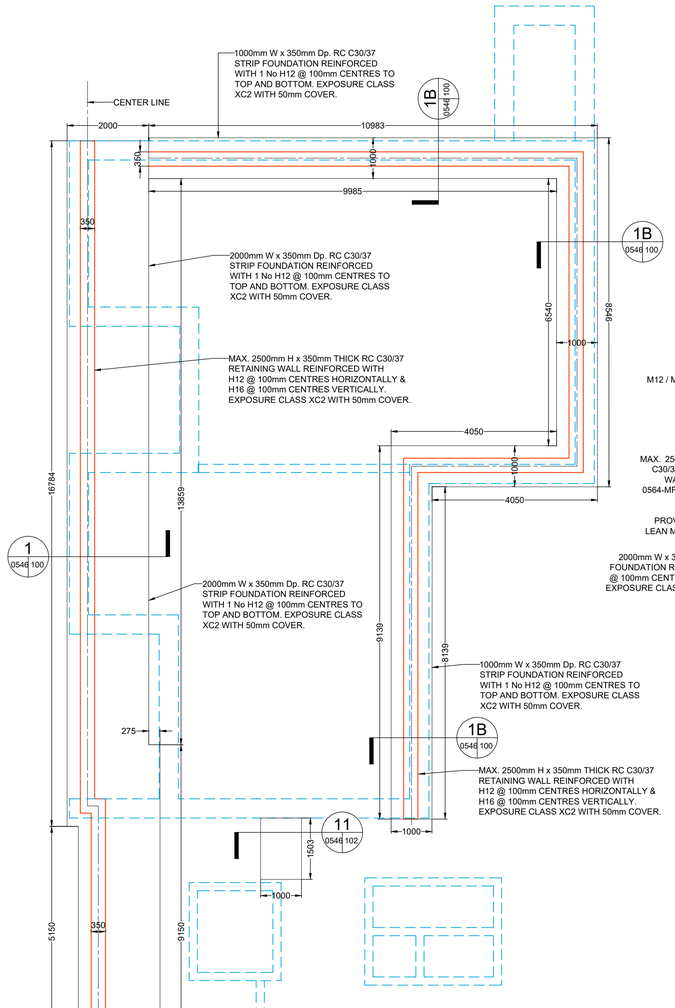


LOWER FOUNDATION PLAN - STRIP & RETAINING WALL


SCALE 1:75 @ A1

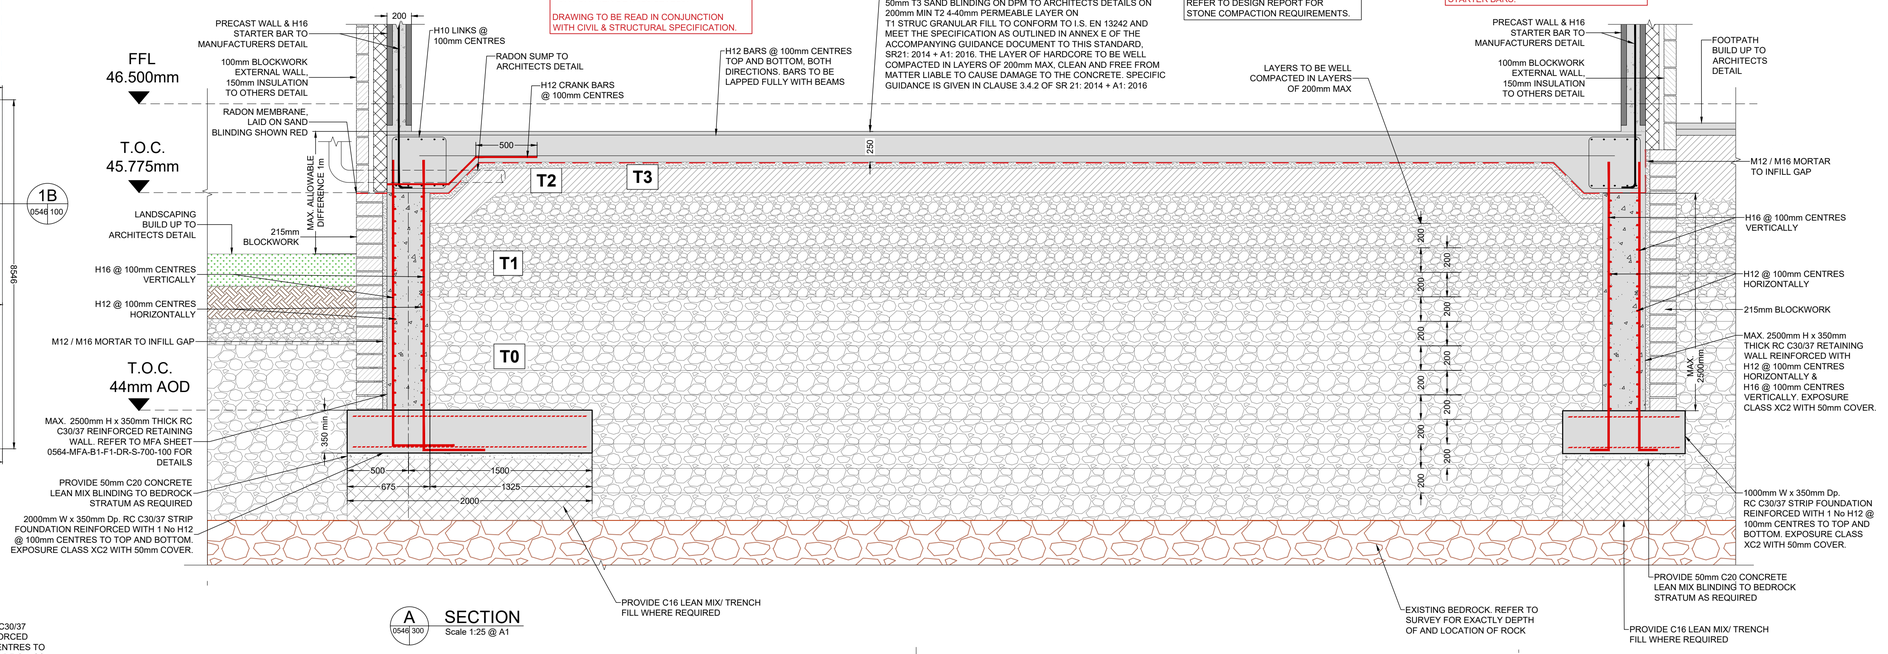


A 0546 300 SECTION
Scale 1:25 @ A1

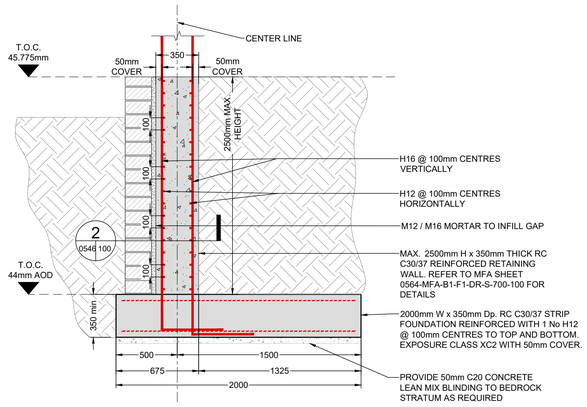


1 0546 100 TYP RETAINING WALL SECTION
Scale 1:25 @ A1

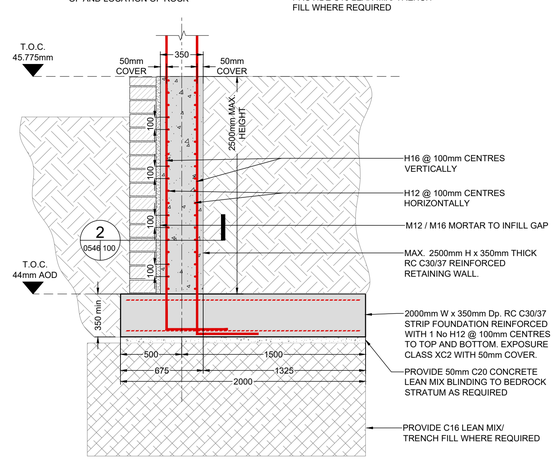

1A 0546 100 TYP RETAINING WALL SECTION
Scale 1:25 @ A1

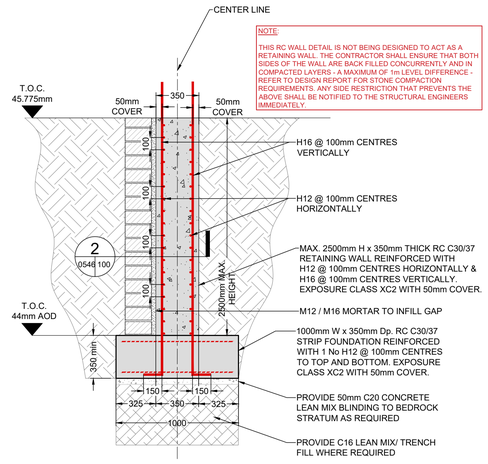

1B 0546 100 TYP RETAINING WALL SECTION
Scale 1:25 @ A1

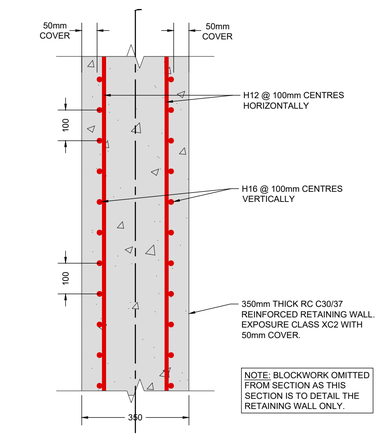

2 0546 100 RETAINING WALL SECTION
Scale 1:10 @ A1